

LAND-STAR

4150 N Hwy 183 LIBERTY HILL, TX 78642

LAND-STAR LLC



PROPERTY OVERVIEW

ADDRESS	4150 N HWY 183 LIBERTY HILL, TX 78642
INTERSECTION	N HWY 183
SCHOOL DISTRICT	Liberty Hill
SITE AREA ACREAGE	35.01 Acres
SITE AREA SFT	1,525,036 SFT
COUNTY / CITY /STATE	WILLIAMSON/LIBERTY HILL/TEXAS
CURRENT ZONING	-
CURRENT USE	RAW LAND
POTENTIAL USES	Residential/ Commercial / Light Industrial
LEGAL DESCRIPTION	AW0415 MCDEVITT, J. SUR., ACRES 35.01

SURVEY



LOCATION MAP
NOT TO SCALE

49.824 AC
JANET Y. ARLITT
(2001041079)

(PORTION OF 204.30 AC TRACT 2094/359
PORTION OF 222.2 AC TRACT 473/152)

N88°19'29"E 684.97'
(N89°40'00"E 685.07')

S88°21'45"W 930.42'

N88°16'29"W 100.56'

67.02'

2218

IN CONC.

FENCE IS 0.5' ON PROPERTY

FENCE IS 0.6' ON PROPERTY

N01°36'39"W 381.16'
(N00°30'00"E 318.17')

12.04 AC
ALAN AND KIMBERLEY SHIELD
(2167/613)

JOHN MCDEVITT SURVEY, ABSTRACT NO. 415

FENCE IS 0.4' OFF PROPERTY

FENCE IS 0.8' OFF PROPERTY

N85°00'59"E 267.86'
(N87°01'30"E 267.86')

N01°48'45"E 648.33'
(N03°45'06"E 648.36')

N13°59'22"E 220.84'
(N15°52'30"E 220.88')

COVERED CONC.

DILAPIDATED BLDG. 17'X18'

PROPANE TANK

COVERED CONC.

10'x16' SHED

GRAVEL DRIVE

WOOD DECK

CONC. WALK

COVERED CONC. PORCH

1 STORY WOOD HOUSE APPROX. 2,031 SQ. FT. BLDG. FOOTPRINT (SEE HOUSE DETAIL FOR DIMENSIONS)

ASPHALT

CONC. DRAINAGE

FENCE IS 0.1' ON PROPERTY

CONC.

24" RCP

101

CONC.

N85°00'20"E 643.47'
(N87°01'00"E 643.52')

S85°03'32"W 689.28'
(S87°03'32"W 689.32')

GRAVEL DRIVE

METAL FENCE IS 1.9' ON PROPERTY

HOG WIRE FENCE IS 0.3' ON PROPERTY

P.O.B.

L1

L5

N. HIGHWAY 183
(100' RIGHT-OF-WAY)

S01°43'31"W 1798.5'

S01°32'13"W 674.92'
(S01°31'31"W 675.24')

ASPHALT

34.990 ACRES
35.01 AC.
RACHEL ALLENBY
(2003047341)

CONC.

IN CONC.

CONC.

1 STORY CONC. BLDG. 35'x24' APPROX. 851 SQ. FT. BLDG. FOOTPRINT

56.1'

L4

METAL FENCE IS 1.8' ON PROPERTY

HOG WIRE FENCE IS 0.4' OFF PROPERTY

HOG WIRE FENCE IS 0.4' ON PROPERTY

N75°02'44"W 349.92'
(N73°02'44"W 349.98')

5283

METAL FENCE IS 0.9' ON PROPERTY

14.031 AC
RISING SPIRIT RV PARK, LLC
(2019123567)

N22°45'59"W 310.86'
(N20°44'30"W 310.77')

METAL FENCE IS 1.2' ON PROPERTY

FENCE IS 0.4' OFF PROPERTY

S77°46'25"W 1204.19'

N88°16'29"W 99.93'

348.20'

20.19 AC
J. PATRICK PROPERTIES, LLC
(2021165221)

(PART OF 204.30 AC TRACT 473/152)

49.824 AC
JANET Y. ARLITT
(2001041079)

(PORTION OF 204.30 AC TRACT 2094/359
PORTION OF 222.2 AC TRACT 473/152)

FENCE IS 0.4' ON PROPERTY

S21°09'41"E 151.43'
(S19°09'00"E 151.79')

HOUSE DETAIL
NOT TO SCALE

20.1'
15.3'
45.7'
32.4'
13.9'
7.0'
16.7'
59.4'

N22°49'15"W 609.44'
(N20°49'00"W 609.83')

BOUNDARY LINE AGREEMENT (1056/532)

(S71°02'30"W 412.33')

S68°59'27"W 784.91'
[S68°58'38"W 785.01']

(S71°00'30"W 371.69')

FENCE IS 0.8' ON PROPERTY

FENCE IS 1.9' ON PROPERTY

FENCE IS 0.5' OFF PROPERTY

L2

L3

100.7609 AC
FM3405 VENTURES LLC
WESLAYAN VENTURES LLC
(2023006756)

LINE TABLE			
LINE	BEARING	DISTANCE	(RECORD)
L1	N03°30'03"E	60.05'	(N05°28'30"E 60.06')
L2	S18°30'17"W	28.25'	(S21°39'30"W 29.30')
L3	S73°32'25"W	51.21'	(S75°36'30"W 51.14')
L4	N11°31'15"E	47.73'	(N13°23'00"E 47.72')
L5	N23°12'36"W	14.52'	

SCALE: 1" = 100'

GRAPHIC SCALE
100 50 0 100

THIS IS A GRID DRAWING.

BEARING BASIS: THE TEXAS COORDINATE SYSTEM OF 1983 (NAD83) (2011) REFERENCE FRAME, CENTRAL ZONE, BASED ON GPS SOLUTIONS FROM THE LOCAL REAL TIME NETWORK (RTN) FOR CHAPARRAL CONTROL POINT "101".

MAG NAIL WITH WASHER SET IN CONCRETE HEADWALL

TEXAS STATE PLANE COORDINATES:
N 10231255.84
E 3068424.08

- ▲ 40D NAIL FOUND
- ◆ CONTROL POINT/BENCHMARK LOCATION
- W WATER METER
- ⊗ WATER VALVE
- ○○ CLEANOUT
- ⊕ WELL LOCATION
- ⌀ UTILITY POLE
- ← GUY WIRE
- —OU— OVERHEAD UTILITIES
- ☼ LIGHT POLE
- T TELEPHONE UTILITY
- ⚠ UNDERGROUND TELEPHONE MARKER
- M MAILBOX
- EDGE OF ASPHALT PAVEMENT
- —o— METAL FENCE
- —///— HOG WIRE FENCE
- ( ) RECORD INFORMATION DOC. NO. 2003047341
- [ ] RECORD INFORMATION DOC. NO. 2023006756

TITLE COMMITMENT NOTE:

COMMITMENT FOR TITLE INSURANCE PREPARED BY:

Fidelity National Title Insurance Company

G.F. No.: ATA-92-17099223005599A Effective Date: 9/7/2023 Issued: 9/14/2023

The surveyor has relied upon the referenced Commitment for Title regarding easements, restrictions, and other matters affecting this property. No additional research was done for the purpose of this survey. Items listed are worded according to the commitment, followed by surveyor's notes and/or observations.

Schedule "B" items contained therein and re-listed below were considered:

1) Restrictive Covenants: Deleted

10g) Easement(s) for the purpose(s) shown below and rights incidental thereto, as granted in a document:
Granted to: Pedernales Electric Cooperative, Inc.
Purpose: electric and telephone lines and appurtenances
Recording No: Volume 516, Page 92, Deed Records of Williamson County, Texas – **may affect, unable to plot from description in deed.**

10h) Terms, conditions and stipulations contained in that certain document
Entitled: Boundary Line Agreement
Recording No: Volume 1056, Page 529, Official Records of Williamson County, Texas
Reference is hereby made to said document for full particulars.
– **Does not affect. Affects a boundary north and east of subject tract.**

10i) Terms, conditions and stipulations contained in that certain document
Entitled: Boundary Line Agreement
Recording No: Volume 1056, Page 532, Official Records of Williamson County, Texas – **subject to, as shown**

10j) Easement(s) for the purpose(s) shown below and rights incidental thereto, as granted in a document:
Granted to: Chisholm Trail Water Supply Corporation
Purpose: water lines and appurtenances
Recording No: Volume 2131, Page 576, Official Records of Williamson County, Texas – **subject to, unable to locate from document**

10k) Easement(s) for the purpose(s) shown below and rights incidental thereto, as granted in a document:
Granted to: Chisholm Trail Special Utility District
Purpose: water lines and appurtenances
Recording No: Document No. 9626814, Official Records of Williamson County, Texas – **subject to, not plottable by description in said document**

10l) Easement(s) for the purpose(s) shown below and rights incidental thereto, as granted in a document:
Purpose: access easement
Recording No: Document No. 9638000, Official Records of Williamson County, Texas – **subject to, not plottable (no description in said Document)**

FLOOD-PLAIN NOTE:

The tract shown hereon lies within Zone "X" (areas determined to be outside the 0.2% annual chance floodplain), as identified by the Federal Emergency Management Agency, National Flood Insurance Program, as shown on map no. 48491C0275E, dated September 26, 2008 & 48491C0235F, dated December 20, 2019, for Williamson County, Texas and Incorporated areas. If the tract is not within an identified special flood hazard area, this flood statement does not imply that the property and/or the structures thereon will be free from flooding or flood damage. This flood statement shall not create liability on the part of the surveyor.

GENERAL SURVEY NOTES:

PROPERTY ADDRESS: 4150 N HWY 183, LIBERTY HILL, TX. 78642

DATE OF SURVEY: October 3, 2023

ATTACHMENTS: Metes and Bounds

SURVEYOR'S CERTIFICATE:

CERTIFIED TO:
Josephine Sarah Allenby
Star Developers LLC
Fidelity National Title Insurance Company
Austin Title Company

I hereby certify that a survey of the property shown hereon was actually made on the ground under my direction and supervision on the date shown, and that to the best of my professional knowledge and belief: there are no apparent encroachments, overlapping of improvements, discrepancies, boundary line conflicts, visible utility lines or roads in place, except as shown hereon, and that this property abuts or adjoins a dedicated road right-of-way or access easement, unless noted hereon.

This survey substantially complies with the current Texas Society of Professional Surveyors Manual of Practice for a Category 1A, Condition 3 Land Title Survey. Effective December 6, 2020.

Paul J. Flugel 10-12-2023
Paul J. Flugel Date
Registered Professional Land Surveyor
State of Texas No. 5096
PaulF@ChapSurvey.com

STATE OF TEXAS REGISTERED PAUL J. FLUGEL 5096 PROFESSIONAL LAND SURVEYOR

Chaparral
Professional Land Surveying, Inc.
Surveying and Mapping

PROJECT NO.: 2056-1
DRAWING NO.: 2056-001-BAS
PLOT DATE: 10/12/2023
PLOT SCALE: 1"=100'
DRAWN BY:

4150 N Hwy 183 LIBERTY HILL, TX 78642
LAND-STAR LLC | +1 214-455-7623 | Venkat@land-star.us | www.land-star.us

GALLERY




HWY 183


Site
Future
Liberty Hill
High School &
Middle School
LARIAT
CHESMAR HOMES
David Weekley Homes
SANTA RITA RANCH
Stonewall Ranch




FM 3405


HWY 183


HWY 183


FM 3405
HWY 183

DRIVE TIME

Walmart Supercenter - 15.2Miles - 23 Min Drive


Georgetown City - 15.6Miles - 25Min Drive

Austin TX - 35Miles - 39Min Drive

Breakway Airport - 18.4Miles - 23Min Drive

Burnet Municipal Airport- 26.6Miles - 34Min Drive

NEIGHBOURHOOD REALESTATE HOMES

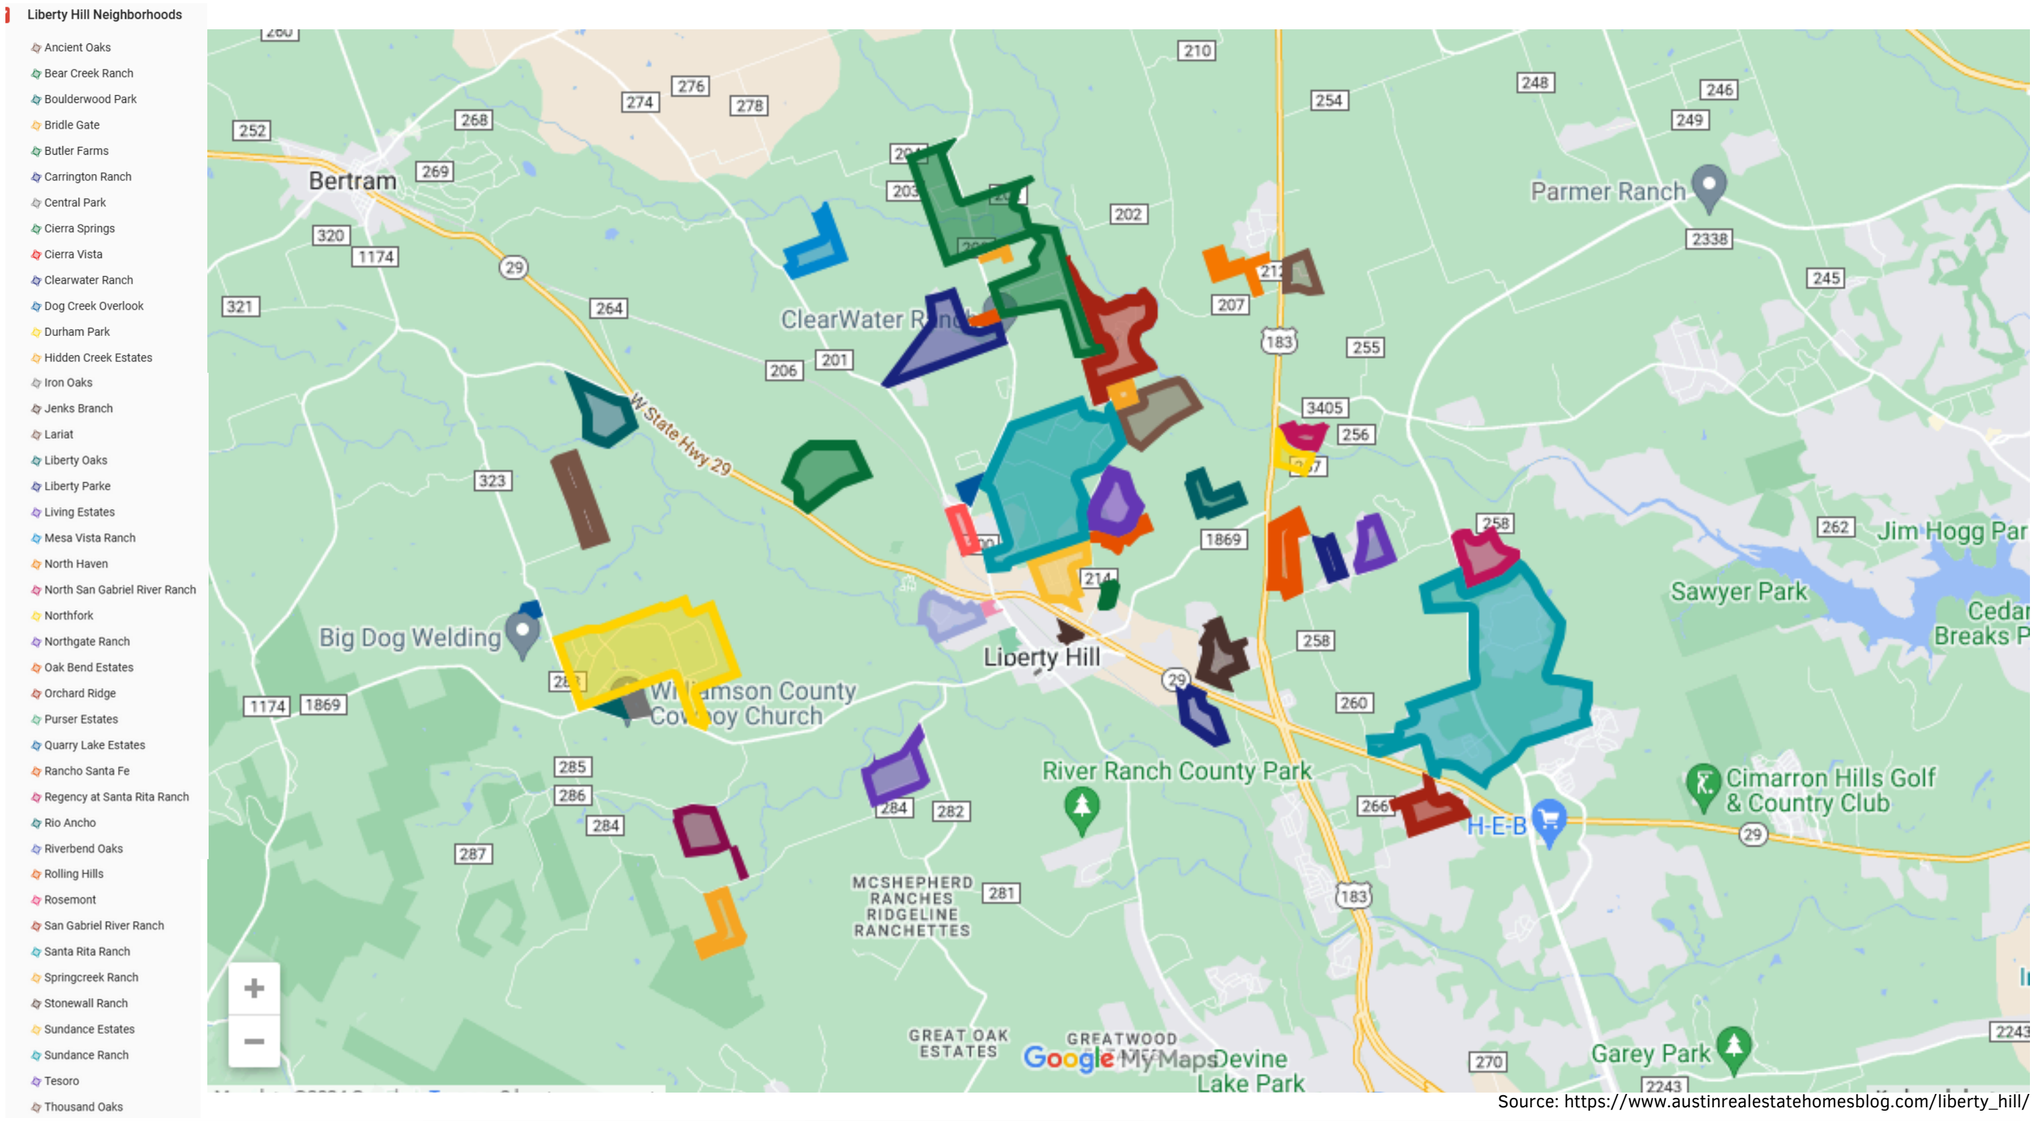

Source: https://www.austinrealestatehomesblog.com/liberty_hill/



VENKAT(VICTOR)GOTTIPATI

214-455-7623

venkat@land-star.us

LAND-STAR

11-2-2015

Information About Brokerage Services

Texas law requires all real estate license holders to give the following information about brokerage services to prospective buyers, tenants, sellers and landlords.

TYPES OF REAL ESTATE LICENSE HOLDERS:

- **A BROKER** is responsible for all brokerage activities, including acts performed by sales agents sponsored by the broker.
- **A SALES AGENT** must be sponsored by a broker and works with clients on behalf of the broker.

A BROKER'S MINIMUM DUTIES REQUIRED BY LAW (A client is the person or party that the broker represents):

- Put the interests of the client above all others, including the broker's own interests;
- Inform the client of any material information about the property or transaction received by the broker;
- Answer the client's questions and present any offer to or counter-offer from the client; and
- Treat all parties to a real estate transaction honestly and fairly.

A LICENSE HOLDER CAN REPRESENT A PARTY IN A REAL ESTATE TRANSACTION:

AS AGENT FOR OWNER (SELLER/LANDLORD): The broker becomes the property owner's agent through an agreement with the owner, usually in a written listing to sell or property management agreement. An owner's agent must perform the broker's minimum duties above and must inform the owner of any material information about the property or transaction known by the agent, including information disclosed to the agent or subagent by the buyer or buyer's agent.

AS AGENT FOR BUYER/TENANT: The broker becomes the buyer/tenant's agent by agreeing to represent the buyer, usually through a written representation agreement. A buyer's agent must perform the broker's minimum duties above and must inform the buyer of any material information about the property or transaction known by the agent, including information disclosed to the agent by the seller or seller's agent.

AS AGENT FOR BOTH - INTERMEDIARY: To act as an intermediary between the parties the broker must first obtain the written agreement of *each party* to the transaction. The written agreement must state who will pay the broker and, in conspicuous bold or underlined print, set forth the broker's obligations as an intermediary. A broker who acts as an intermediary:

- Must treat all parties to the transaction impartially and fairly;
- May, with the parties' written consent, appoint a different license holder associated with the broker to each party (owner and buyer) to communicate with, provide opinions and advice to, and carry out the instructions of each party to the transaction.
- Must not, unless specifically authorized in writing to do so by the party, disclose:
  - that the owner will accept a price less than the written asking price;
  - that the buyer/tenant will pay a price greater than the price submitted in a written offer; and
  - any confidential information or any other information that a party specifically instructs the broker in writing not to disclose, unless required to do so by law.

AS SUBAGENT: A license holder acts as a subagent when aiding a buyer in a transaction without an agreement to represent the buyer. A subagent can assist the buyer but does not represent the buyer and must place the interests of the owner first.

TO AVOID DISPUTES, ALL AGREEMENTS BETWEEN YOU AND A BROKER SHOULD BE IN WRITING AND CLEARLY ESTABLISH:

- The broker's duties and responsibilities to you, and your obligations under the representation agreement.
- Who will pay the broker for services provided to you, when payment will be made and how the payment will be calculated.

LICENSE HOLDER CONTACT INFORMATION: This notice is being provided for information purposes. It does not create an obligation for you to use the broker's services. Please acknowledge receipt of this notice below and retain a copy for your records.

Land-Star Real Estate LLC	9005447	victor@land-star.us	972-900-5391
Licensed Broker /Broker Firm Name or Primary Assumed Business Name	License No.	Email	Phone
Kurosh Bian	0466341214	kuroshbian@yahoo.com	214-683-5815
Designated Broker of Firm	License No.	Email	Phone
Venkat (Victor) Gottipati	0541319	victor@land-star.us	214-455-7623
Licensed Supervisor of Sales Agent/ Associate	License No.	Email	Phone
Sales Agent/Associate's Name	License No.	Email	Phone

Buyer/Tenant/Seller/Landlord Initials _____ _____ Date _____