

LAND-STAR

HWY 79, 300 CR 354 GAUSE TEXAS 77857

LAND-STAR

Latitude and Longitude: 30.797141, -96.700164


ADDRESS	HWY 79 300, CR 354 GAUSE TX 77857
INTERSECTION	HIGHWAY 79/ CR 354
SCHOOL DISTRICT	GAUSE ISD
SITE AREA ACREAGE	178.11 Acres
SITE AREA SFT	7,758,472 SFT
COUNTY / CITY /STATE	GAUSE/MILAM/TEXAS
CURRENT ZONING	-
CURRENT USE	RAW LAND
POTENTIAL USES	Residential/ Commercial
LEGAL DESCRIPTION	A3870 WEBB, AZRA,178.11 ACRES,(PT IN AB 164)

VENKAT(VICTOR)GOTTIPATI | VENKAT@RE-STAR.US

SURVEY

LAND-STAR

VENKAT(VICTOR)GOTTIPATI | VENKAT@RE-STAR.US

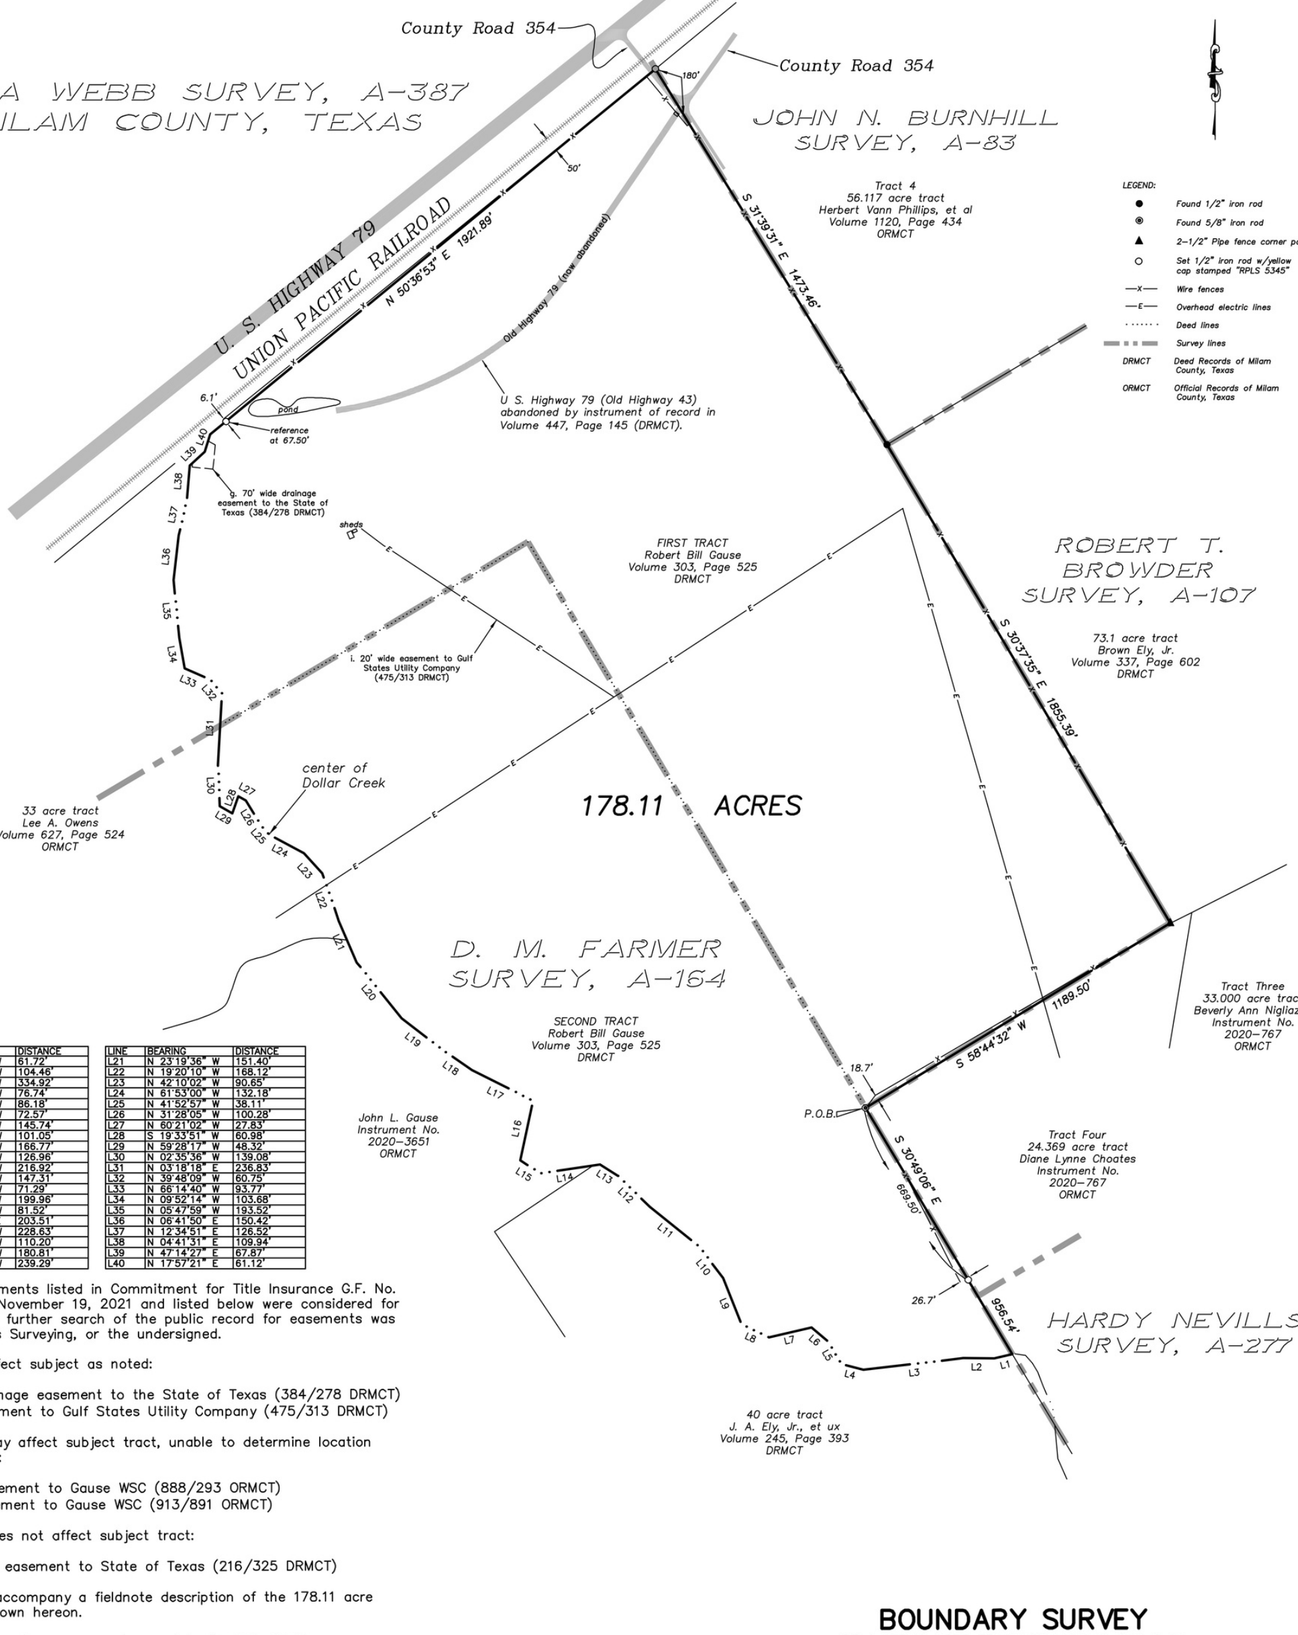

LINE	BEARING	DISTANCE
L1	S 75° 11'37" W	61.72'
L2	[illegible] 7'10" W	104.46'
L3	S 83° 2'15" W	334.92'
L4	[illegible] 8'30" W	76.74'
L5	[illegible] 5'32" W	86.18'
L6	[illegible] 34'36" W	72.57'
L7	[illegible] 9'57" W	145.74'
L8	[illegible] 4'08" W	101.05'
L9	[illegible] 2'58" W	166.77'
L10	N 36°56'35" W	126.96'
L11	N 50°53'23" W	216.92'
L12	[illegible] 5'00" W	147.31'
L13	N 57°41'18" W	71.29'
L14	[illegible] 7'42" W	199.96'
L15	[illegible] 4'56" W	81.52'
L16	[illegible] 4'41" E	203.51'
L17	[illegible] 7'42" W	228.53'
L18	N 55°40'29" W	110.20'
L19	N 52°32'41" W	180.81'
L20	N 38°42'31" W	239.29'

LINE	BEARING	DISTANCE
L21	N 23°19'36" W	151.40'
L22	N 19°20'10" W	168.12'
L23	N 42°10'02" W	90.65'
L24	N 61°53'00" W	132.18'
L25	N 41°52'57" W	38.11'
L26	N 31°28'05" W	100.28'
L27	N 60°21'02" W	27.83'
L28	S 19°33'51" W	60.98'
L29	N 59°28'17" W	48.32'
L30	N 02°35'36" W	139.08'
L31	N 03°18'18" E	236.83'
L32	N 39°48'09" W	60.75'
L33	N 68°14'40" W	93.77'
L34	N 09°52'14" W	103.68'
L35	N 05°47'59" W	193.52'
L36	N 08°41'50" E	150.42'
L37	N 12°34'51" E	126.52'
L38	N 04°41'31" E	109.94'
L39	N 47°14'27" E	67.87'
L40	N 17°57'21" E	61.12'

Only those easements listed in Commitment for Title Insurance G.F. No. 21-351, issued November 19, 2021 and listed below were considered for this survey. No further search of the public record for easements was made by Hughes Surveying, or the undersigned.

The following affect subject as noted:

g. 70' wide drainage easement to the State of Texas (384/278 DRMCT)
i. 20' wide easement to Gulf States Utility Company (475/313 DRMCT)

The following may affect subject tract, unable to determine location from description:

m. 15' wide easement to Gause WSC (888/293 ORMCT)
n. 15' wide easement to Gause WSC (913/891 ORMCT)

The following does not affect subject tract:

d. right-of-way easement to State of Texas (216/325 DRMCT)

This plat is to accompany a fieldnote description of the 178.11 acre tract of land shown hereon.

All bearings shown hereon are referenced to Geodetic North.

I, Don Randall Hughes, do hereby certify that this plat correctly represents a survey made on the ground under my direction and supervision on May 25, 2021.

Don Randall Hughes Registered Professional Land Surveyor No. 5345

STATE OF TEXAS REGISTERED DON RANDALL HUGHES 5345 PROFESSIONAL LAND SURVEYOR

Revised November 24, 2021: Addressed title commitment.

BOUNDARY SURVEY

OF A 178.11 ACRE TRACT OF LAND IN THE D. M. FARMER SURVEY, A-164 AND AZRA WEBB SURVEY, ABSTRACT NO. 387, MILAM COUNTY, TEXAS

Hughes Surveying
Texas Board of Professional Engineers and Land Surveyors, Firm Number 10055300
P. O. BOX 1135
212 N. CENTRAL AVENUE
CAMERON, TEXAS 76520
PHONE (254) 697-3646 FAX (254) 697-8776

DATE:	5-25-21
Proj. No.	6802
Drn. By	LEM
Scale:	1"=300'
Dwg No.	C-1379
SHT.	1 OF 1

LAND-STAR

GALLERY








VENKAT(VICTOR)GOTTIPATI | VENKAT@RE-STAR.US

LAND-STAR

Highlights

- *Positioned within the HWY 79 High Growth Industrial Corridor,*
- *Close to Rockdale Alcoa Aluminum Plan Land which is planned for the biggest Industrial Park in Texas.*
- *Close to Byran- College Station Metroplex and Adjoining Highway which is Suitable for Industrial, Storage.*
- *Straight Hwy Drive to Samsung Chip Plant and Tyler Logistics Park.*

VENKAT(VICTOR)GOTTIPATI | VENKAT@RE-STAR.US



LAND-STAR

VENKAT(VICTOR)GOTTIPATI

214-455-7623

venkat@re-star.us